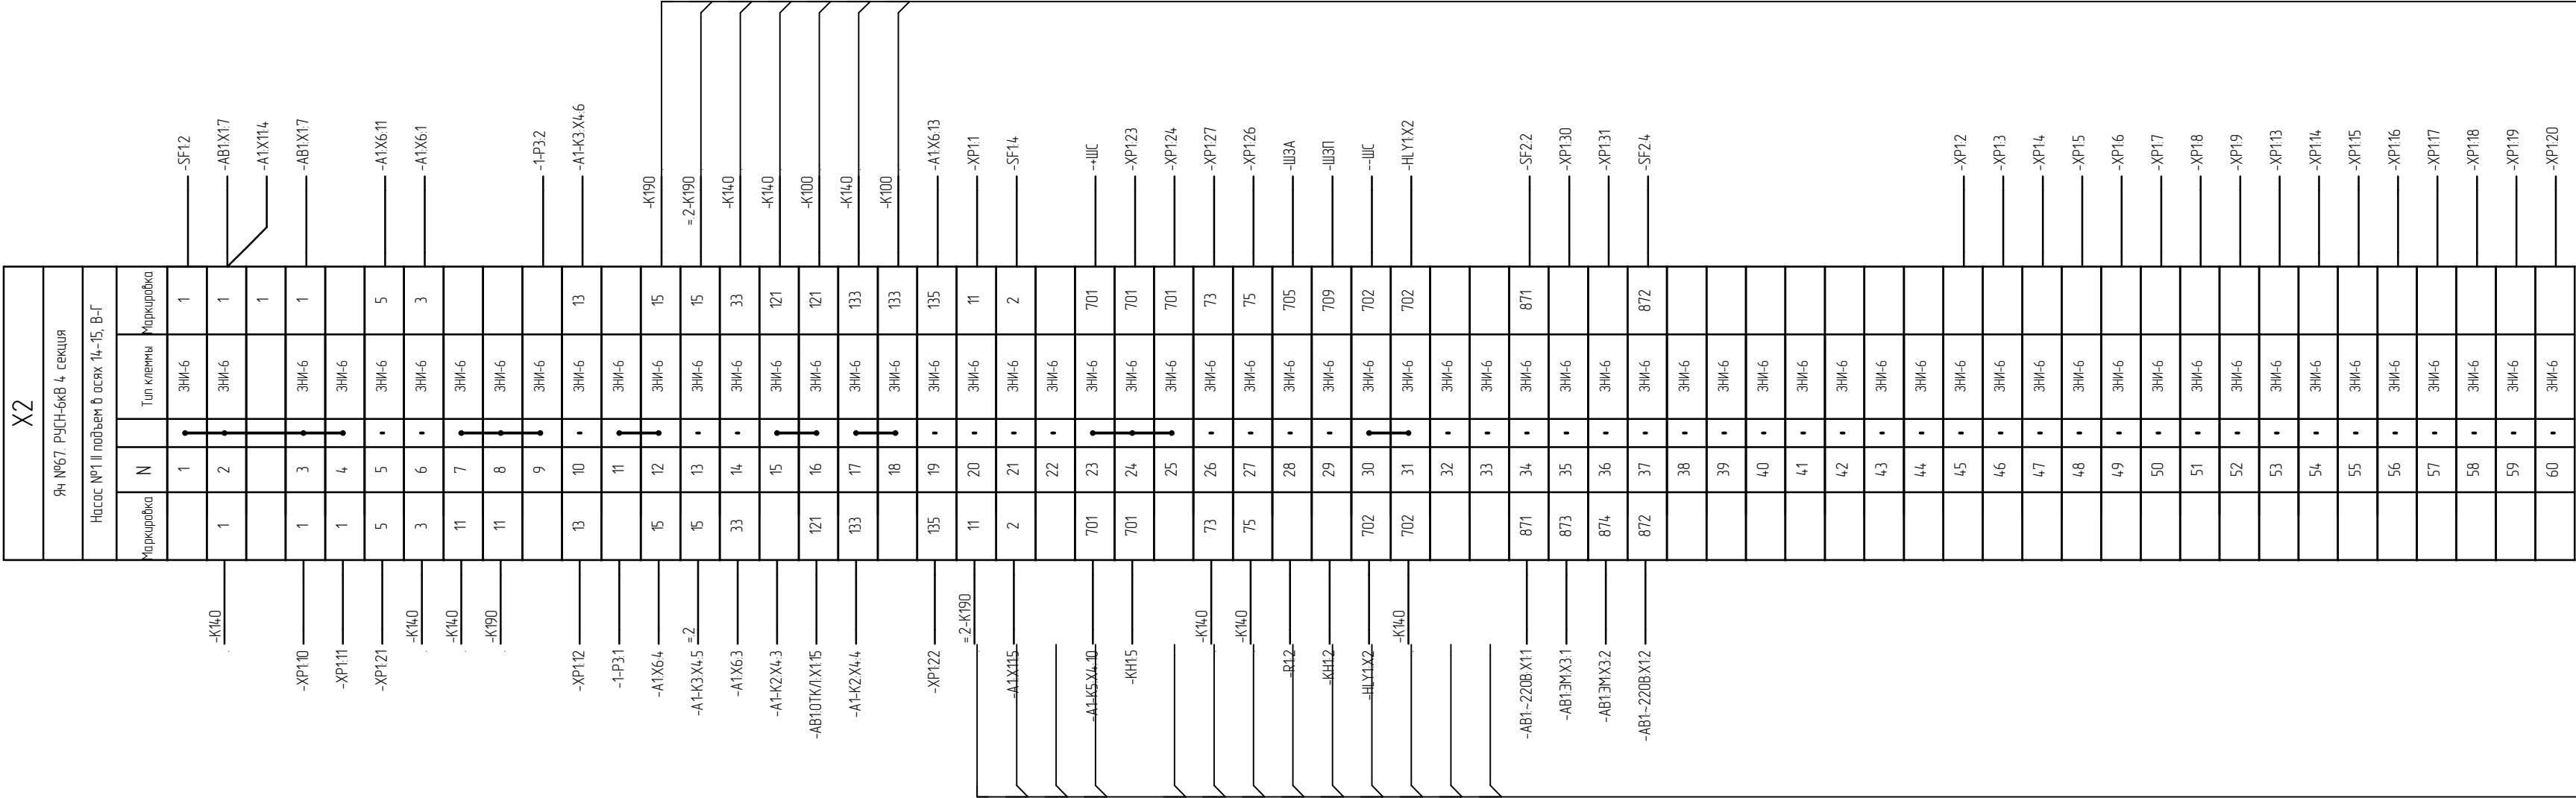


						6128.26-ЭМ2			
						Филиал "Бийскэнерго" АО "СГК-Алтай". Главный корпус			
Изм.	Колуч.	Лист	№ докум	Подп.	Дата	Техническое перевооружение МЗУ	Стадия	Лист	Листов
Разраб	Зиновьев			<i>Зиновьев</i>	08.26		Р	8.1	
Проверил	Келлер В				08.26				
Нач. сектора	Клепиков				08.26	Щит котла №10. Схема электрическая подключения рядов зажимов			
ГИП	Мыльников				08.26				