


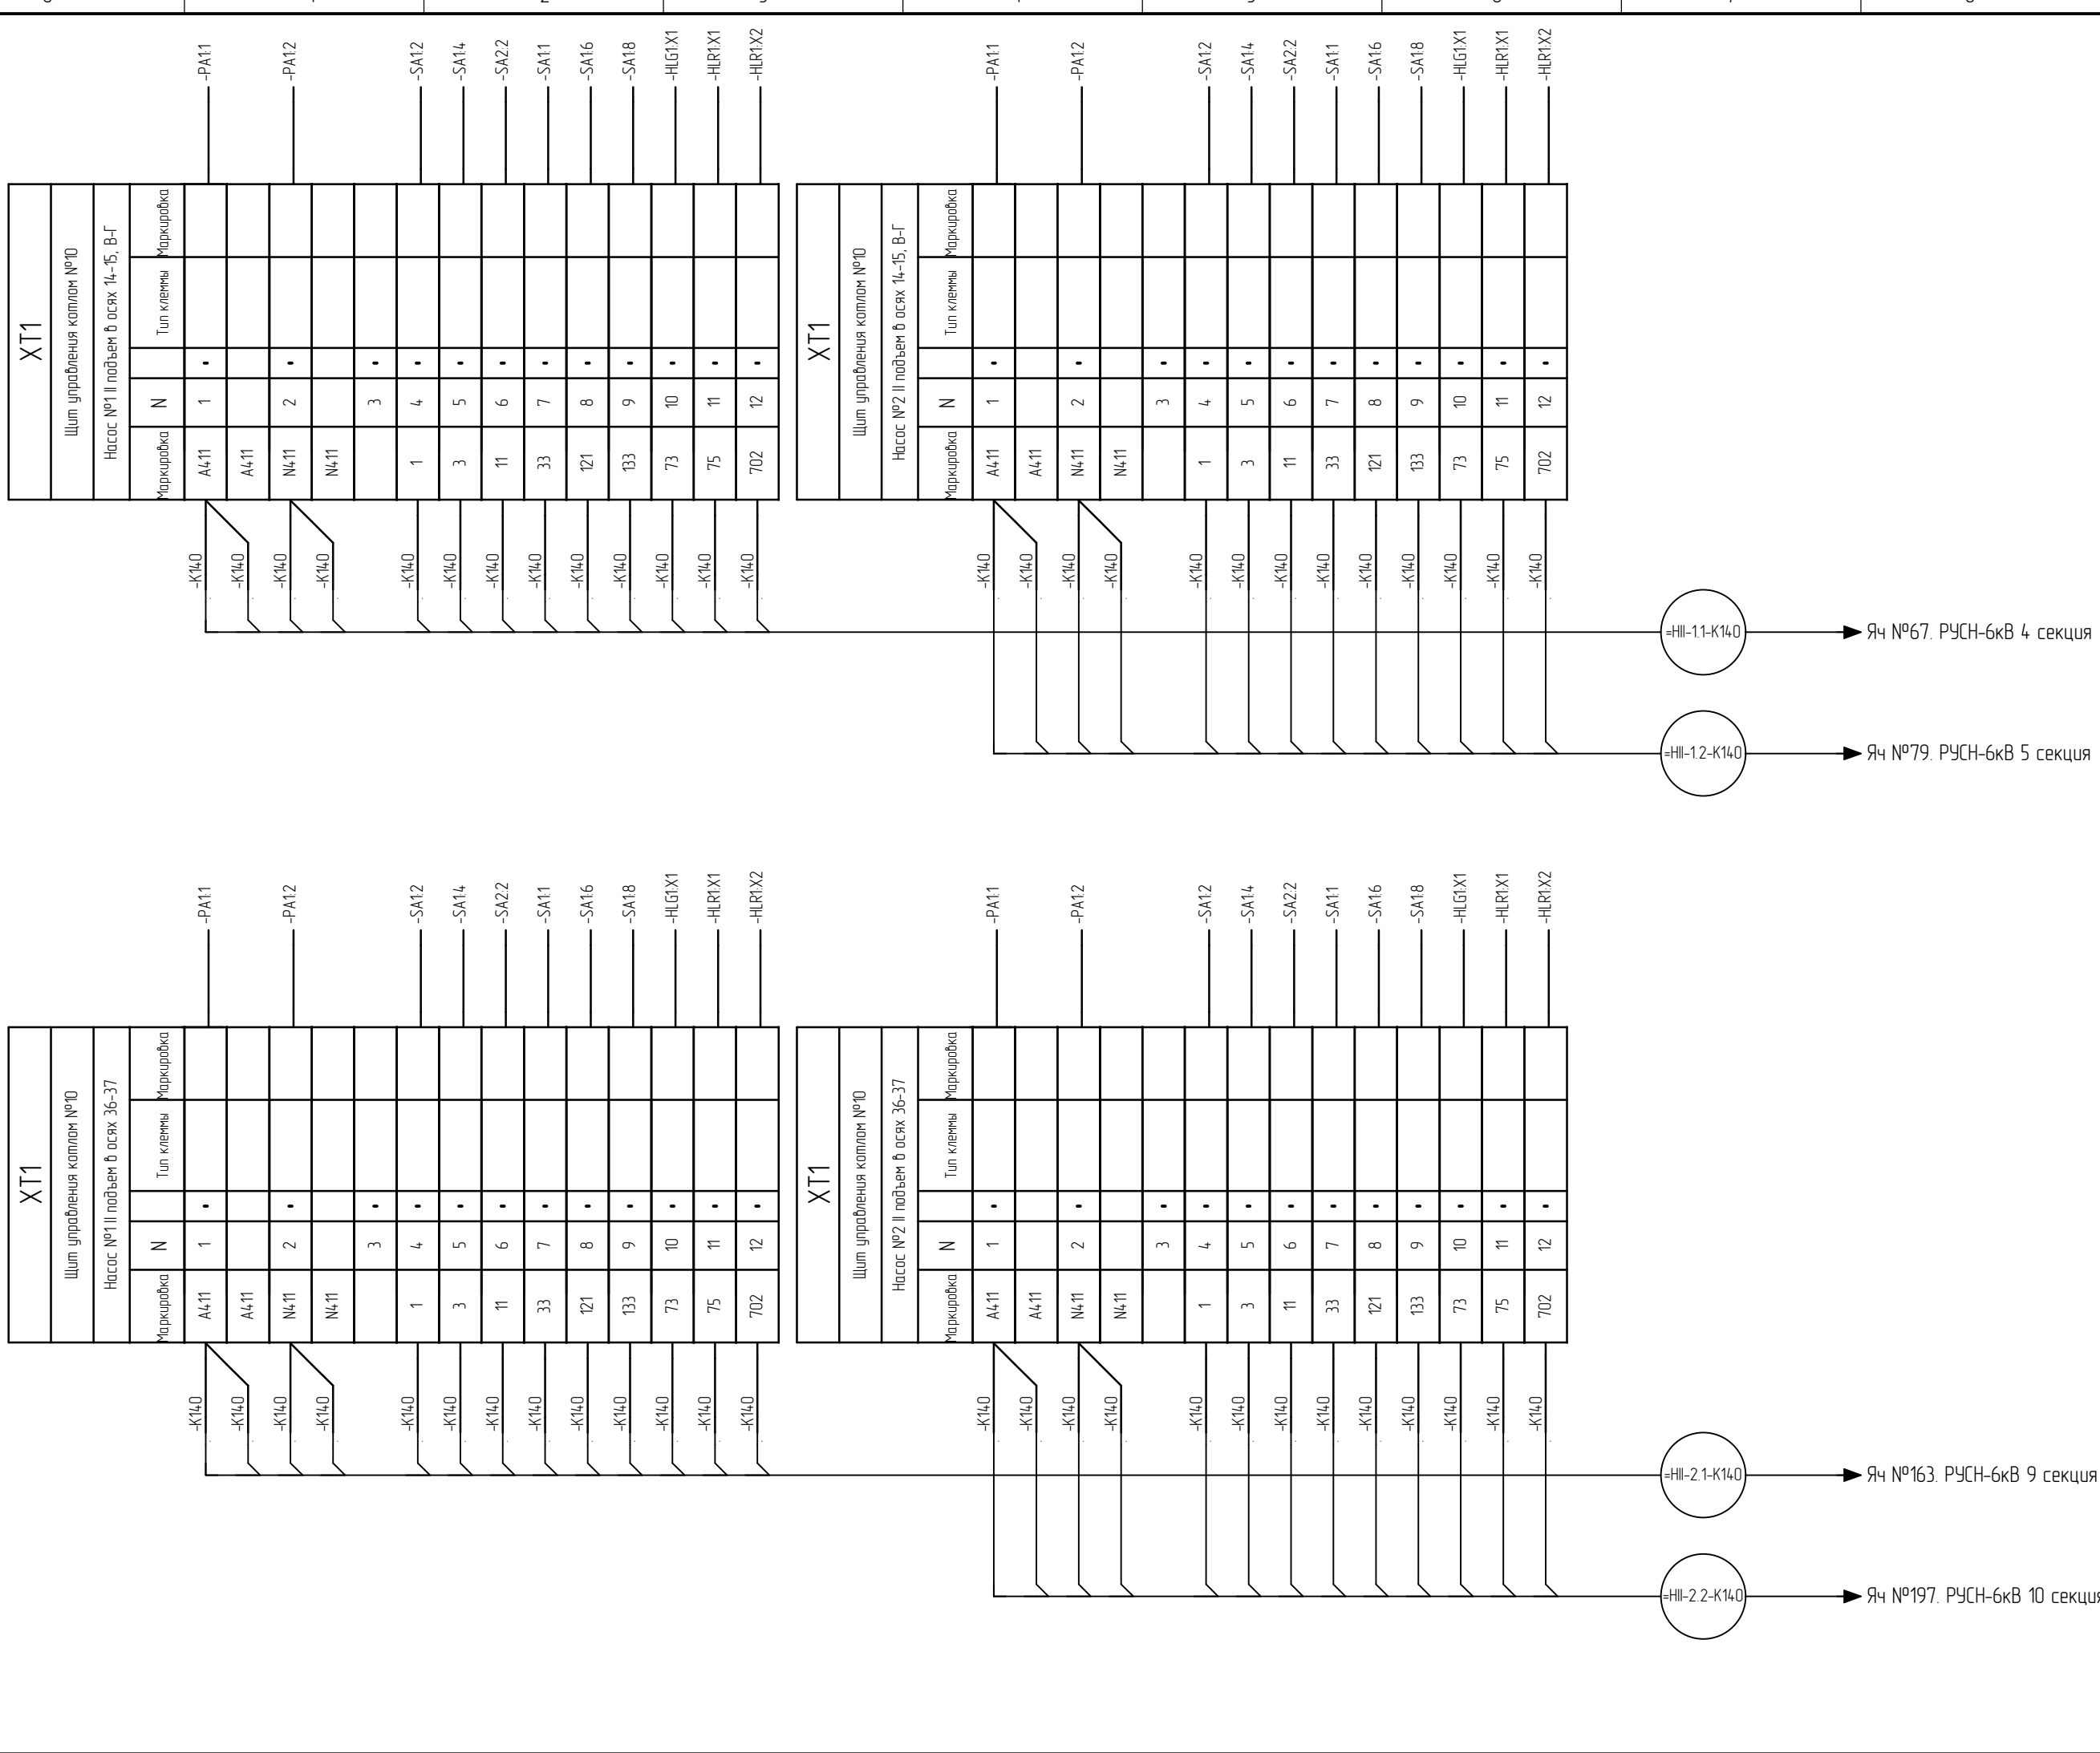

						6128.26-ЭМ2			
						Филиал "Бийскэнерго" АО "СГК-Алтай". Главный корпус			
Изм.	Колуч.	Лист	№ докум.	Подп.	Дата	Техническое перевооружение МЗУ	Стадия	Лист	Листов
Разраб	Зиновьев			<i>Зиновьев</i>	08.26		Р	8	
Проверил	Келлер В			<i>Келлер В</i>	08.26	Щит котла №10. Схема электрическая подключения рядов зажимов	ОБЩЕСТВО С ОГРАНИЧЕННОЙ ОТВЕТСТВЕННОСТЬЮ ОБЩЕСТВЕННАЯ КОМПАНИЯ СИБИРСКИЙ ИНЖЕНЕРНО-ПРОЕКТИРОВАТЕЛЬСКИЙ ЦЕНТР		
Нач. сектора	Клепикова			<i>Клепикова</i>	08.26				
ГИП	Мыльникова			<i>Мыльникова</i>	08.26				