


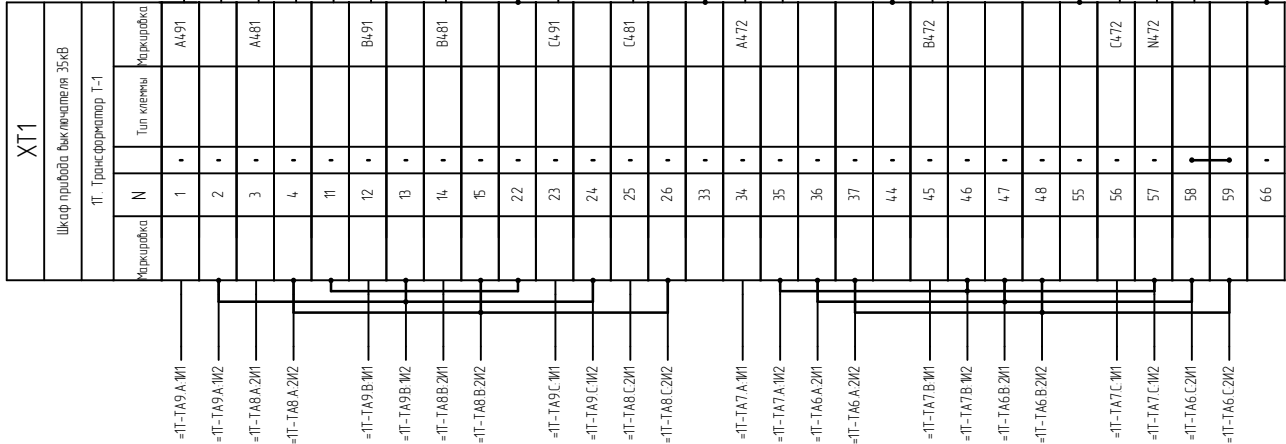

=ПТ-К141 → ШЗТ. Шкаф защиты трансформатора Т-1. ШЭ2607 195

=ПТ-К142 → ШЗТ. Шкаф защиты трансформатора Т-1. ШЭ2607 195

=ПТ-К143 → ШЗТ. Шкаф защиты трансформатора Т-1. ШЭ2607 195

							600126-РЗА		
							Замена трансформатора Т-1 ТД-20000/35 на Барнаульской ТЭЦ-2 АО "СГК-Алтай"		
Изм.	Колуч.	Лист	№ докум.	Подп.	Дата	Релейная защита и автоматика трансформатора Т-1	Стадия	Лист	Листов
Разработал	Зиновьев				07.26		Р	12	2
Проверил	Клепиков				07.26				
Нач.сектора	Клепиков				07.26				
Нконтр.	Клепиков				07.26	Шкаф привода выключателя 35кВ. Схема рядов зажимов			